

HET KNOOPPUNT

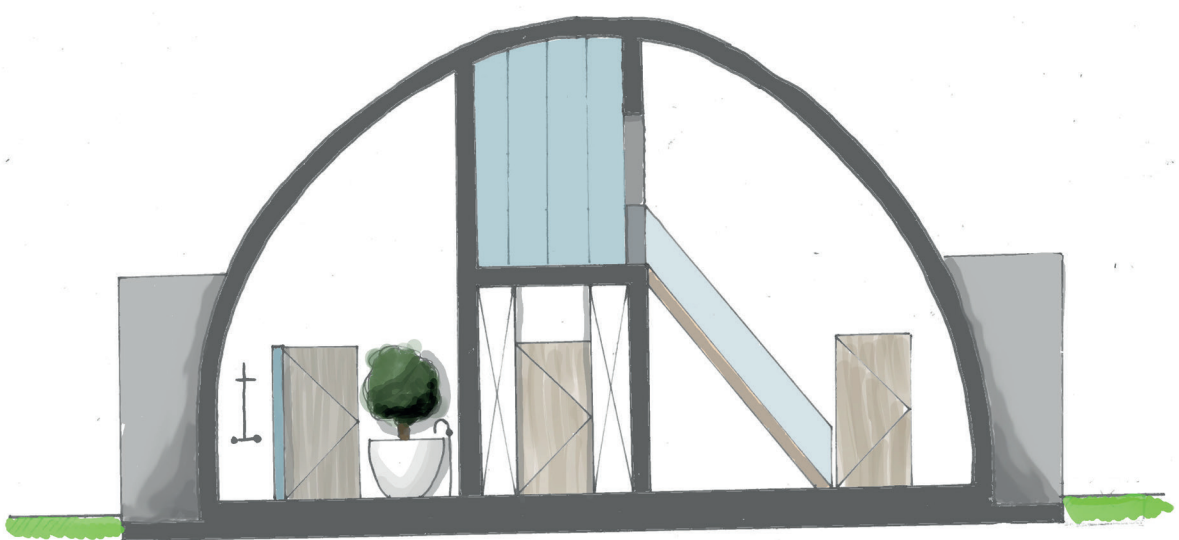
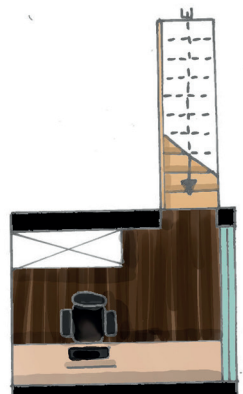
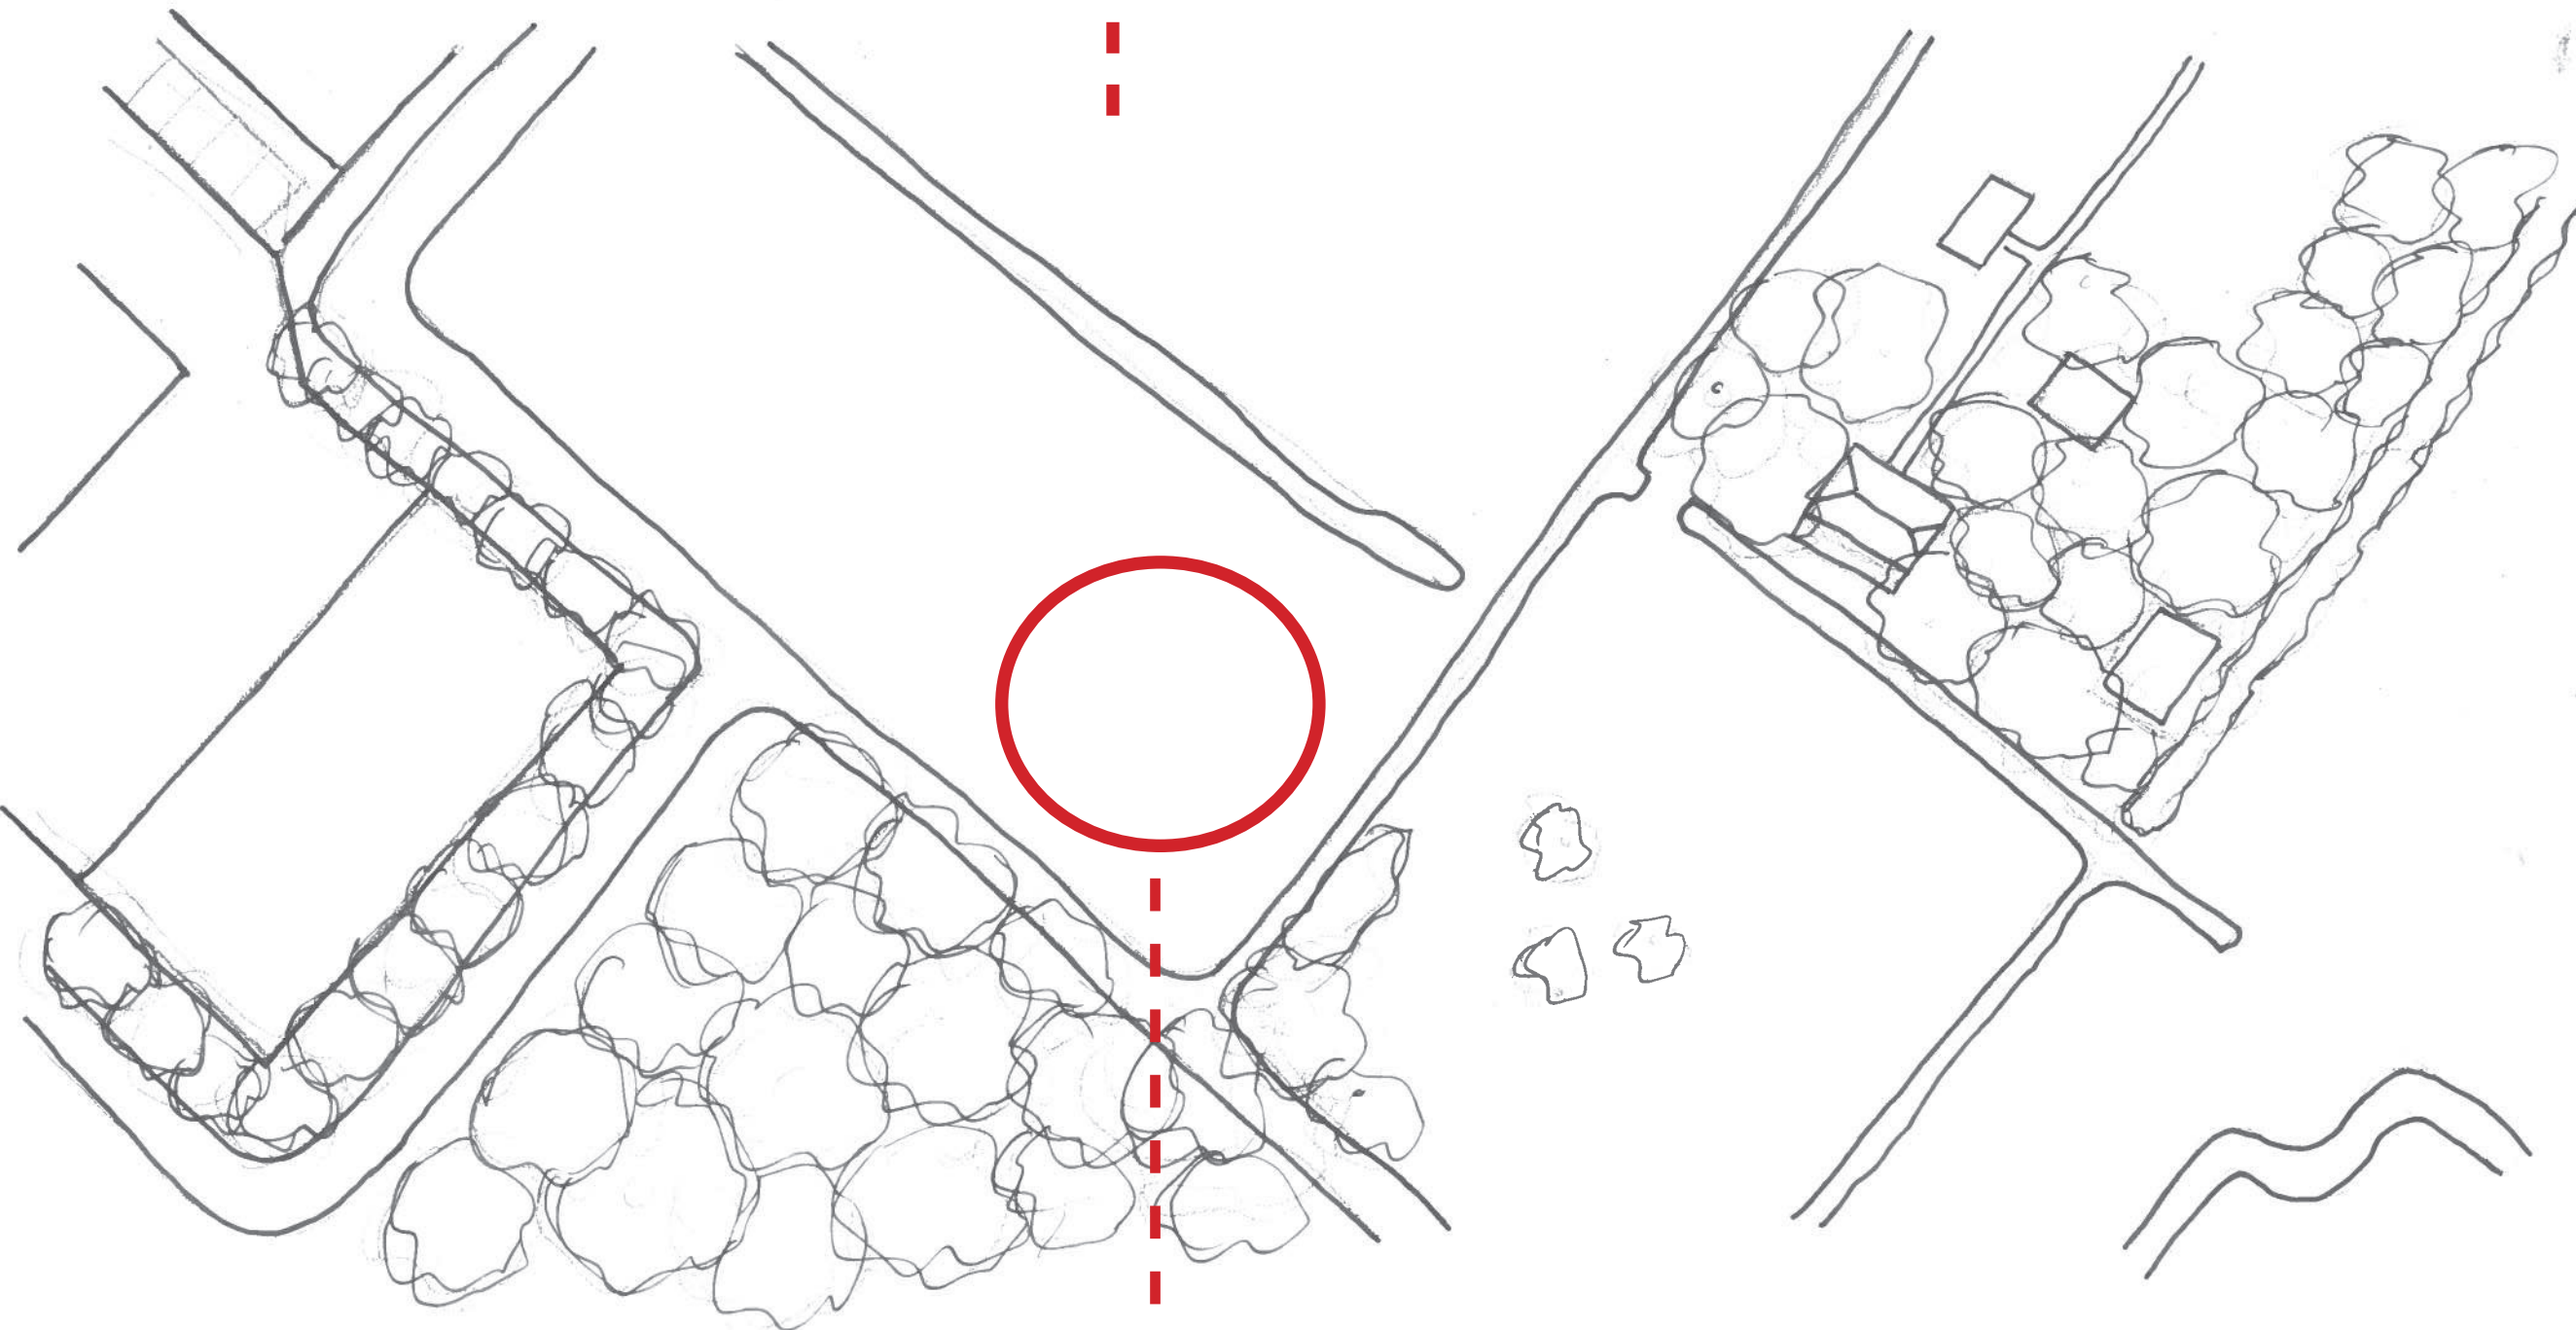
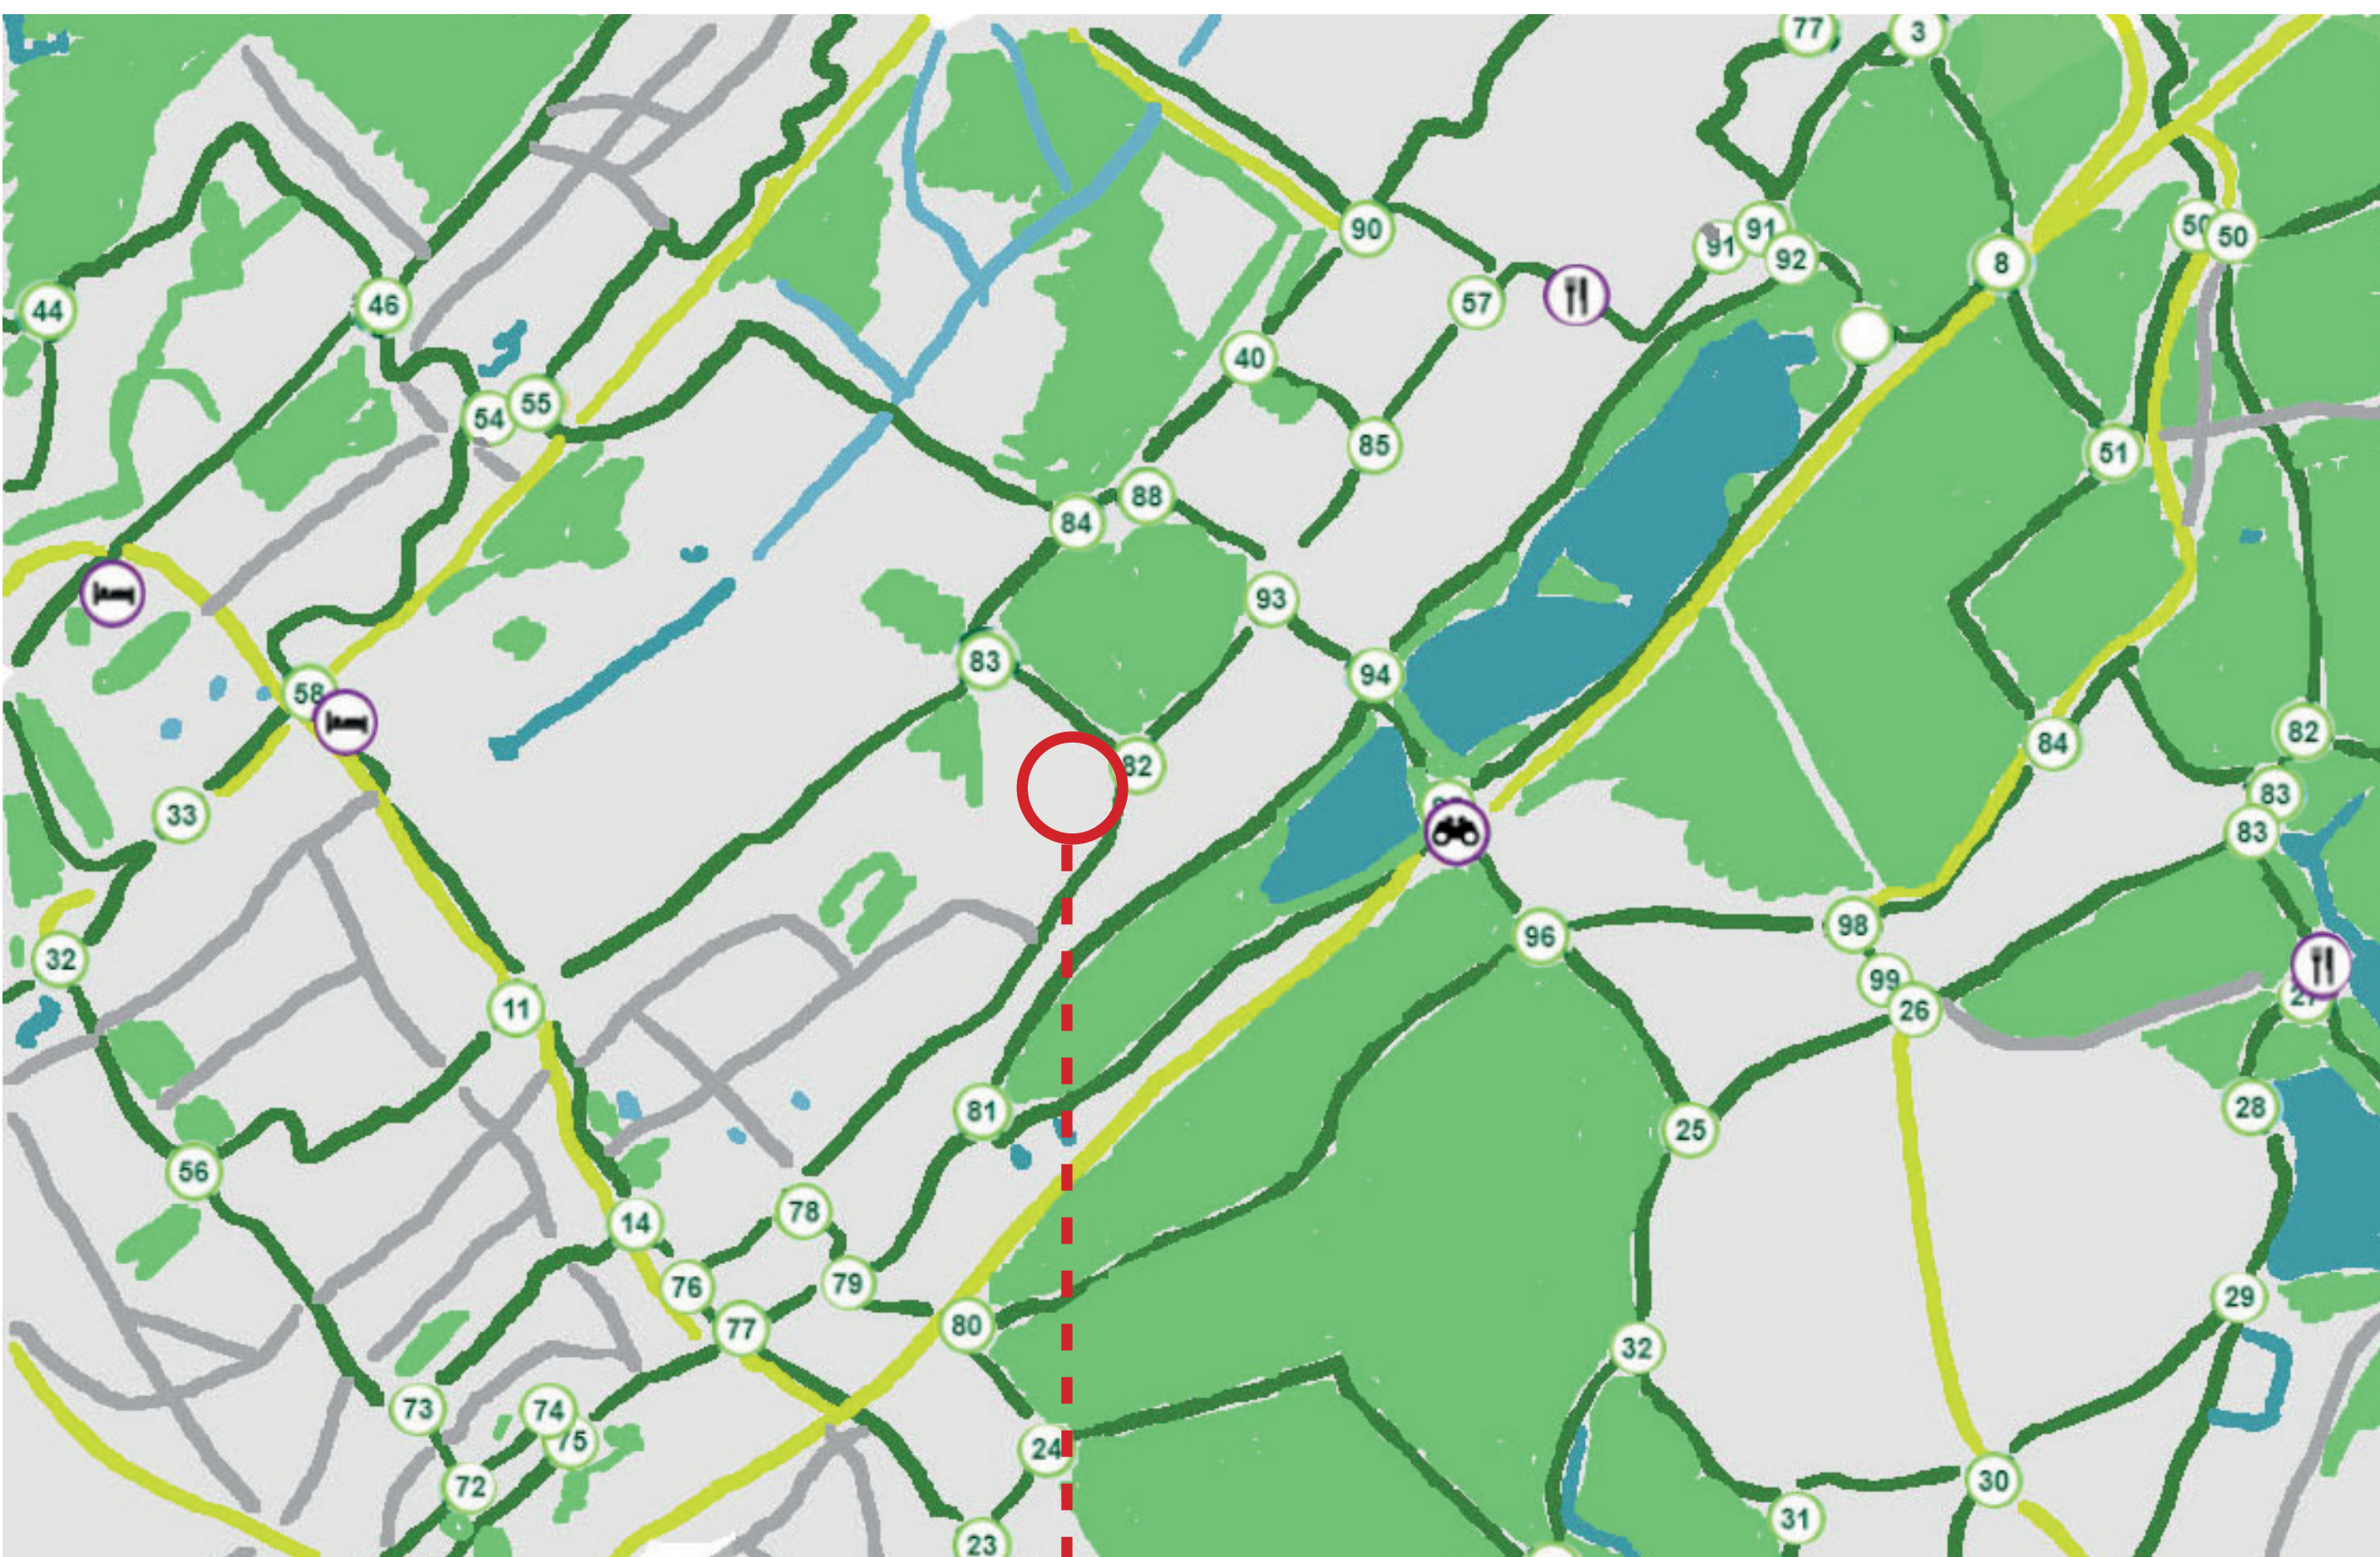


Diagram 41

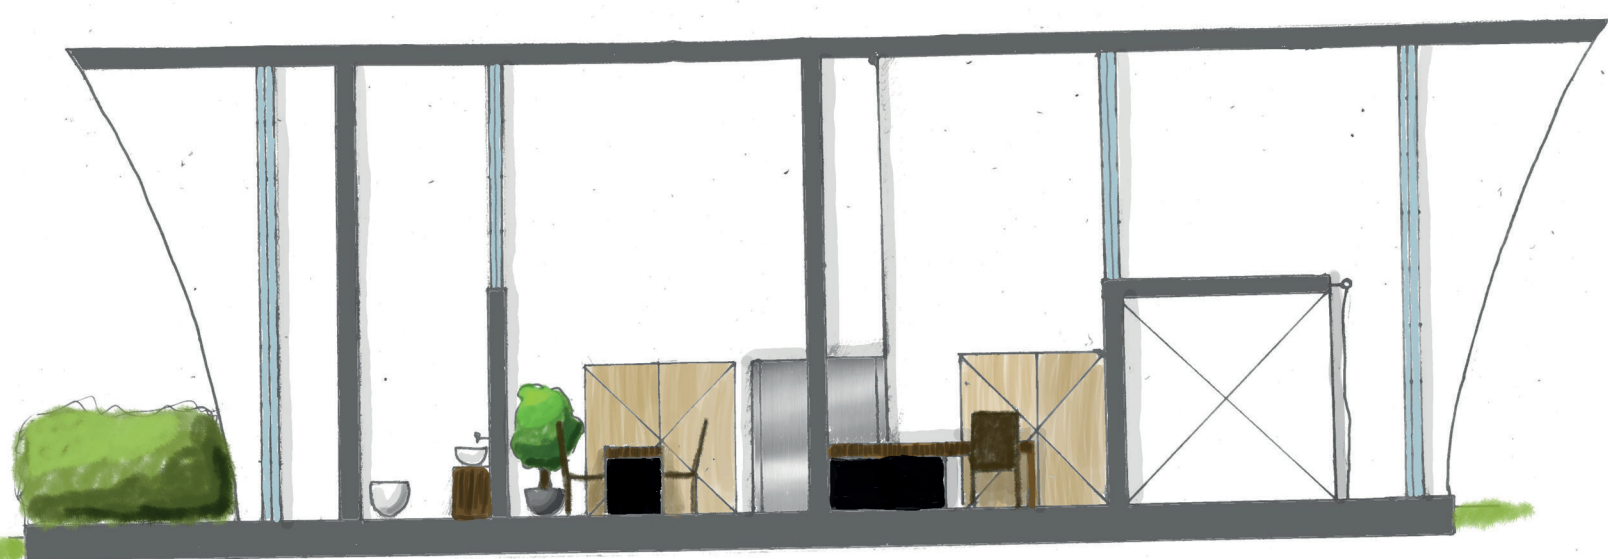


Diagram 42

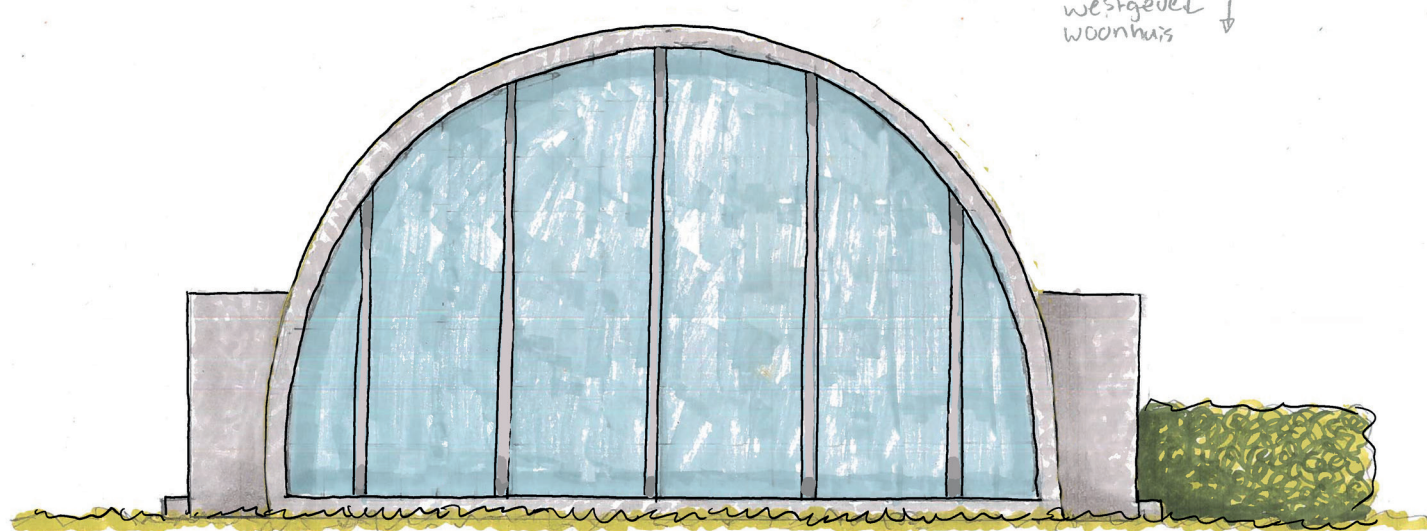


Diagram 43




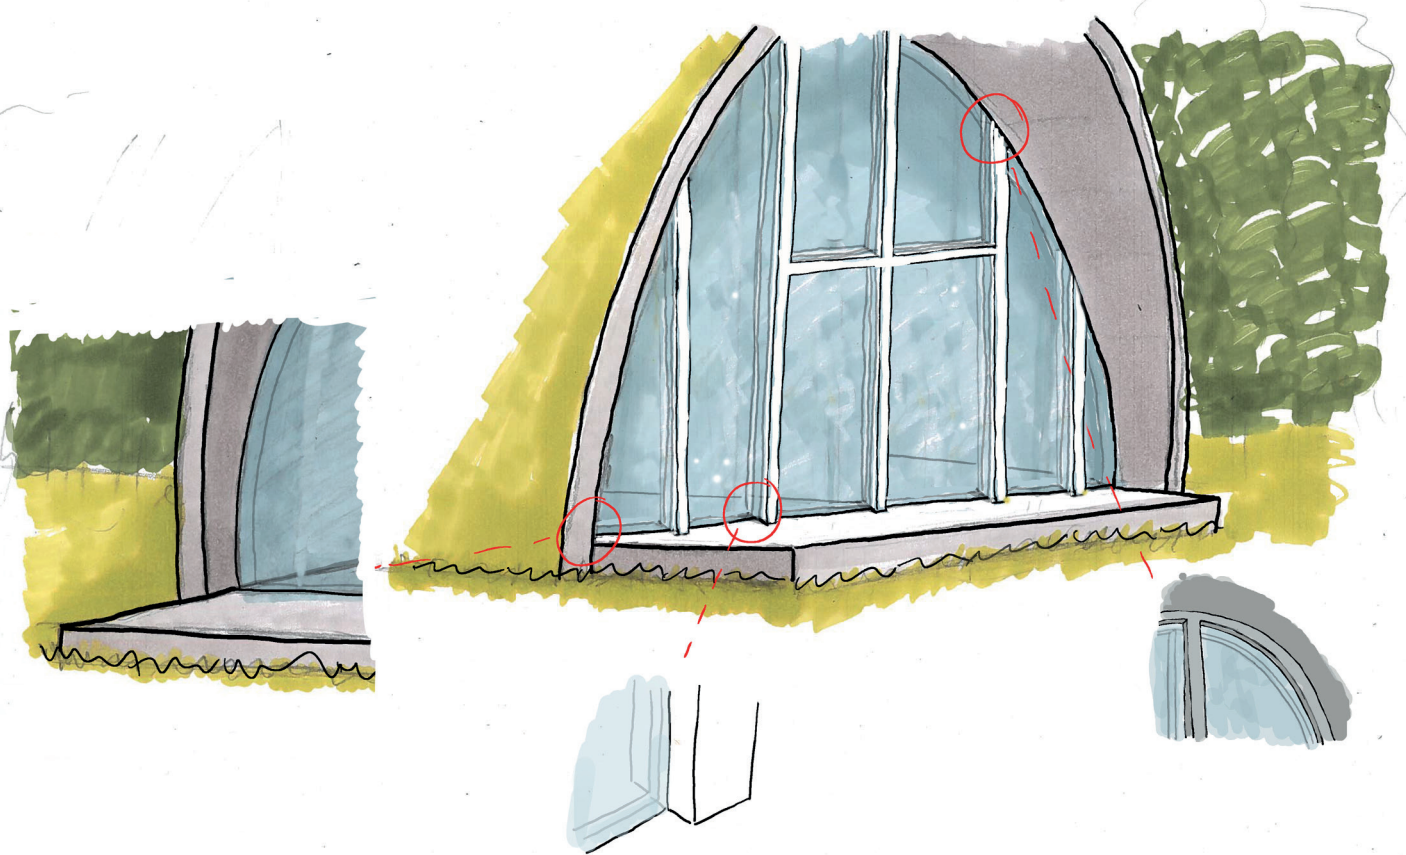


Diagram 44

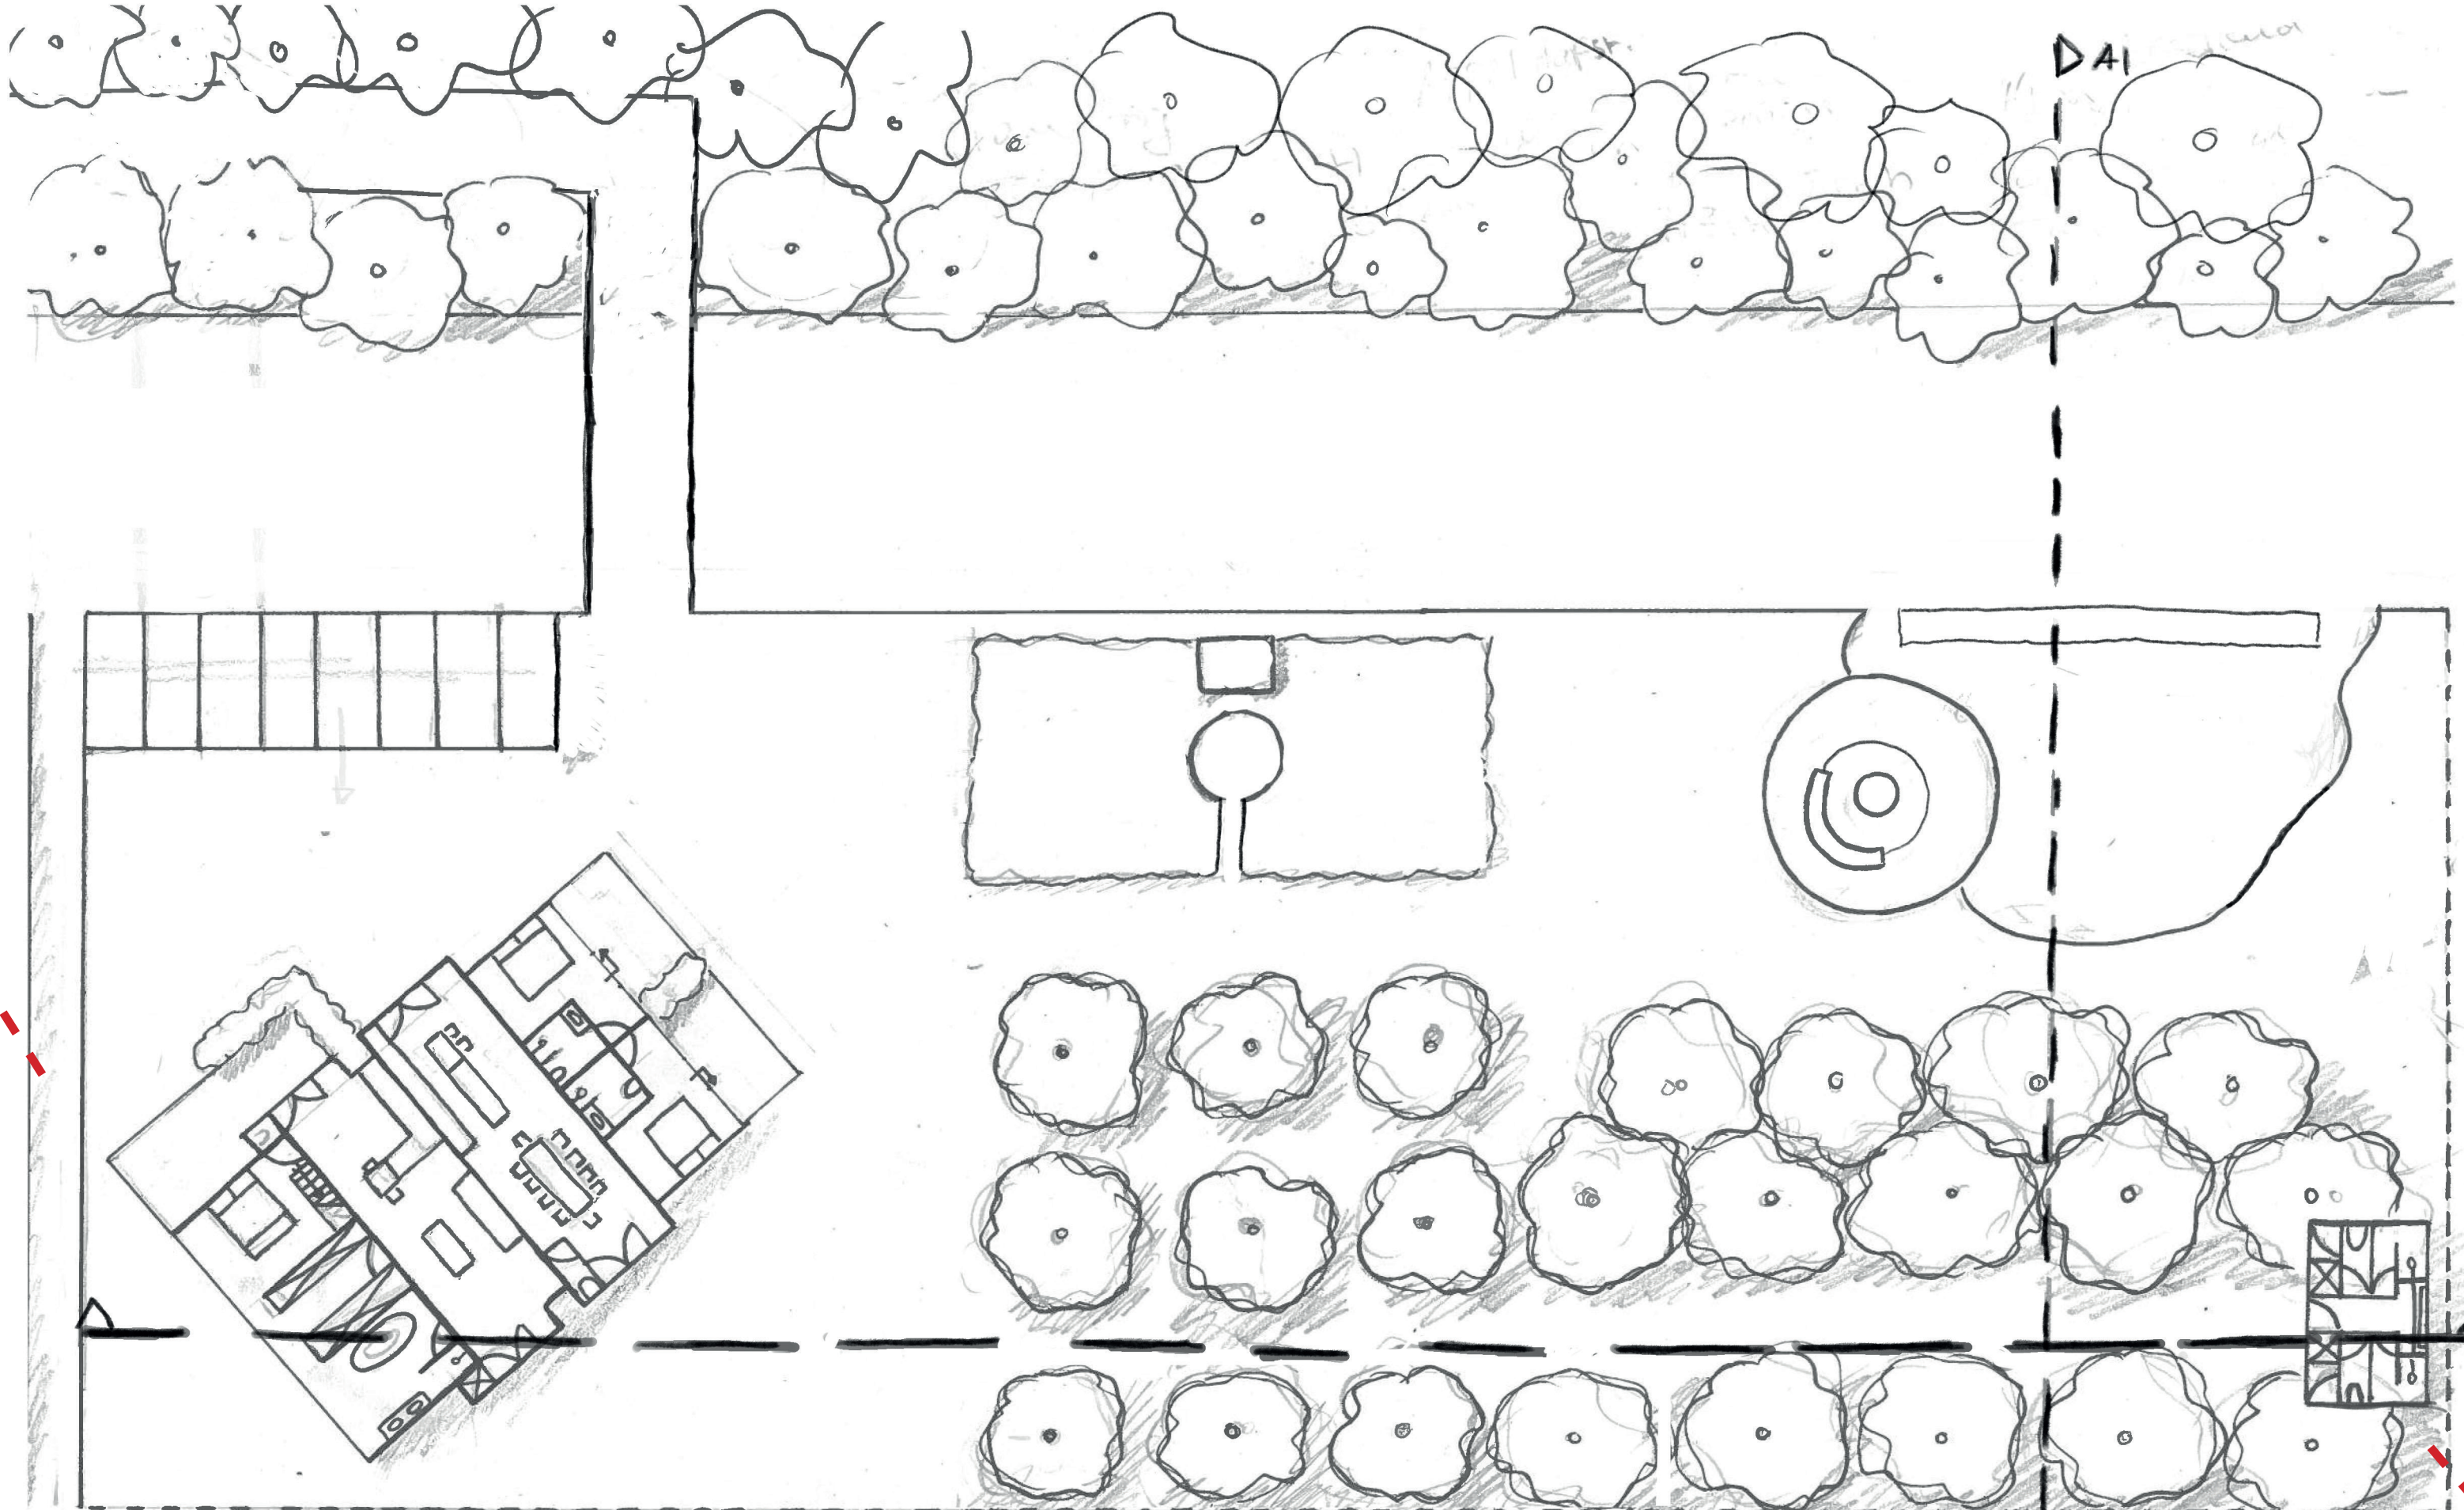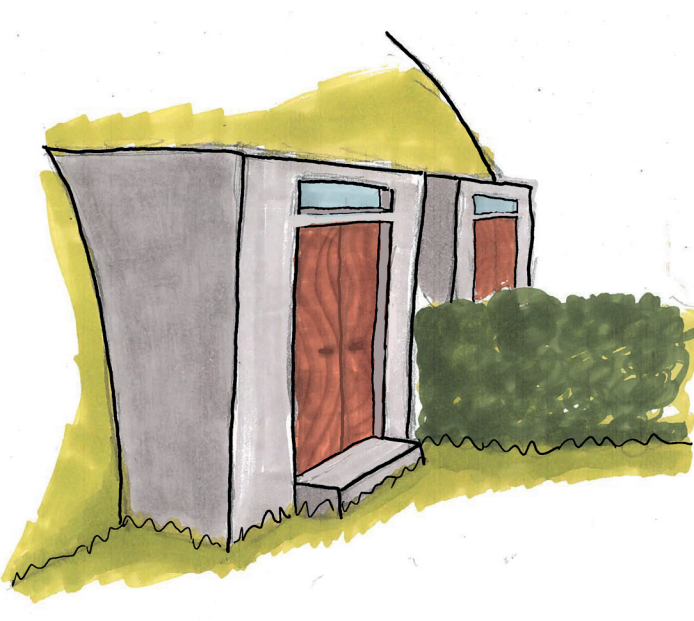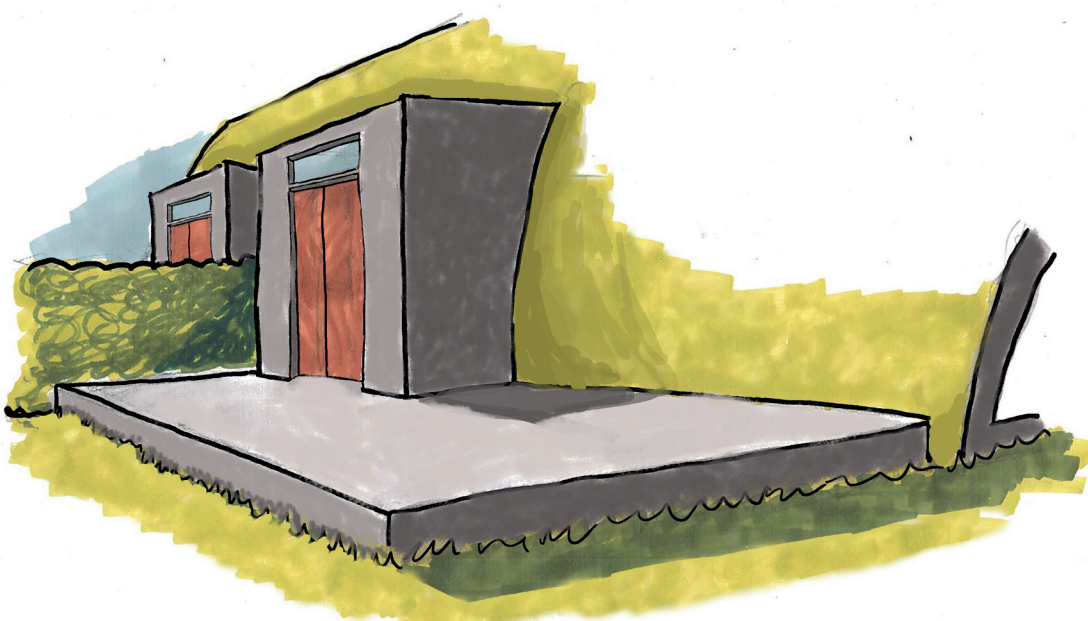

School 1:200
plattegrond Ewin


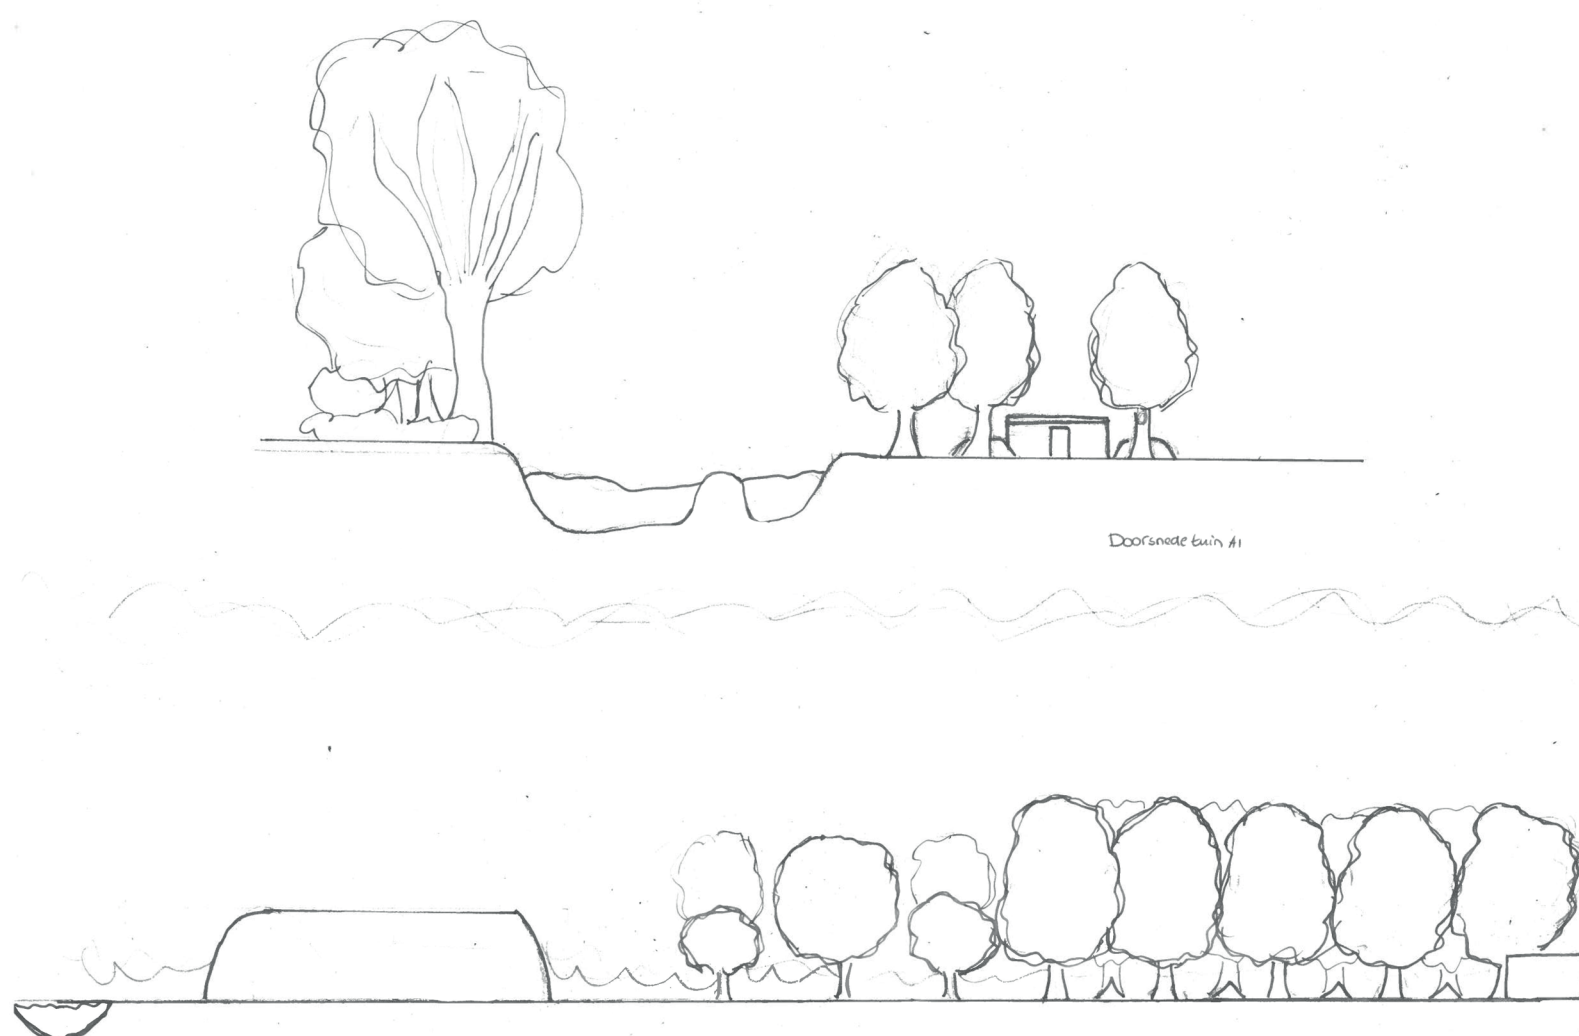


Diagram 45



School 1:370
plattegrond

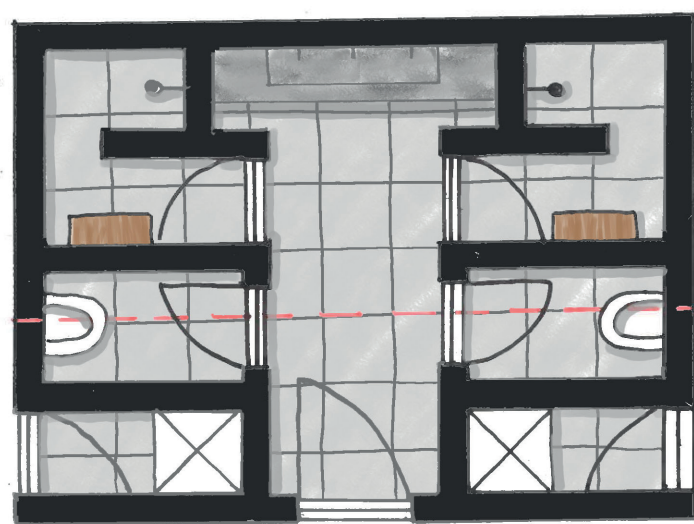